



LEGENDE

- Mur voile en béton armé
- Poteau (Po)
- Joint de dilatation 2cm
- Rds : Raidisseur
- Arase fini
- Radier général
- Epaisseur

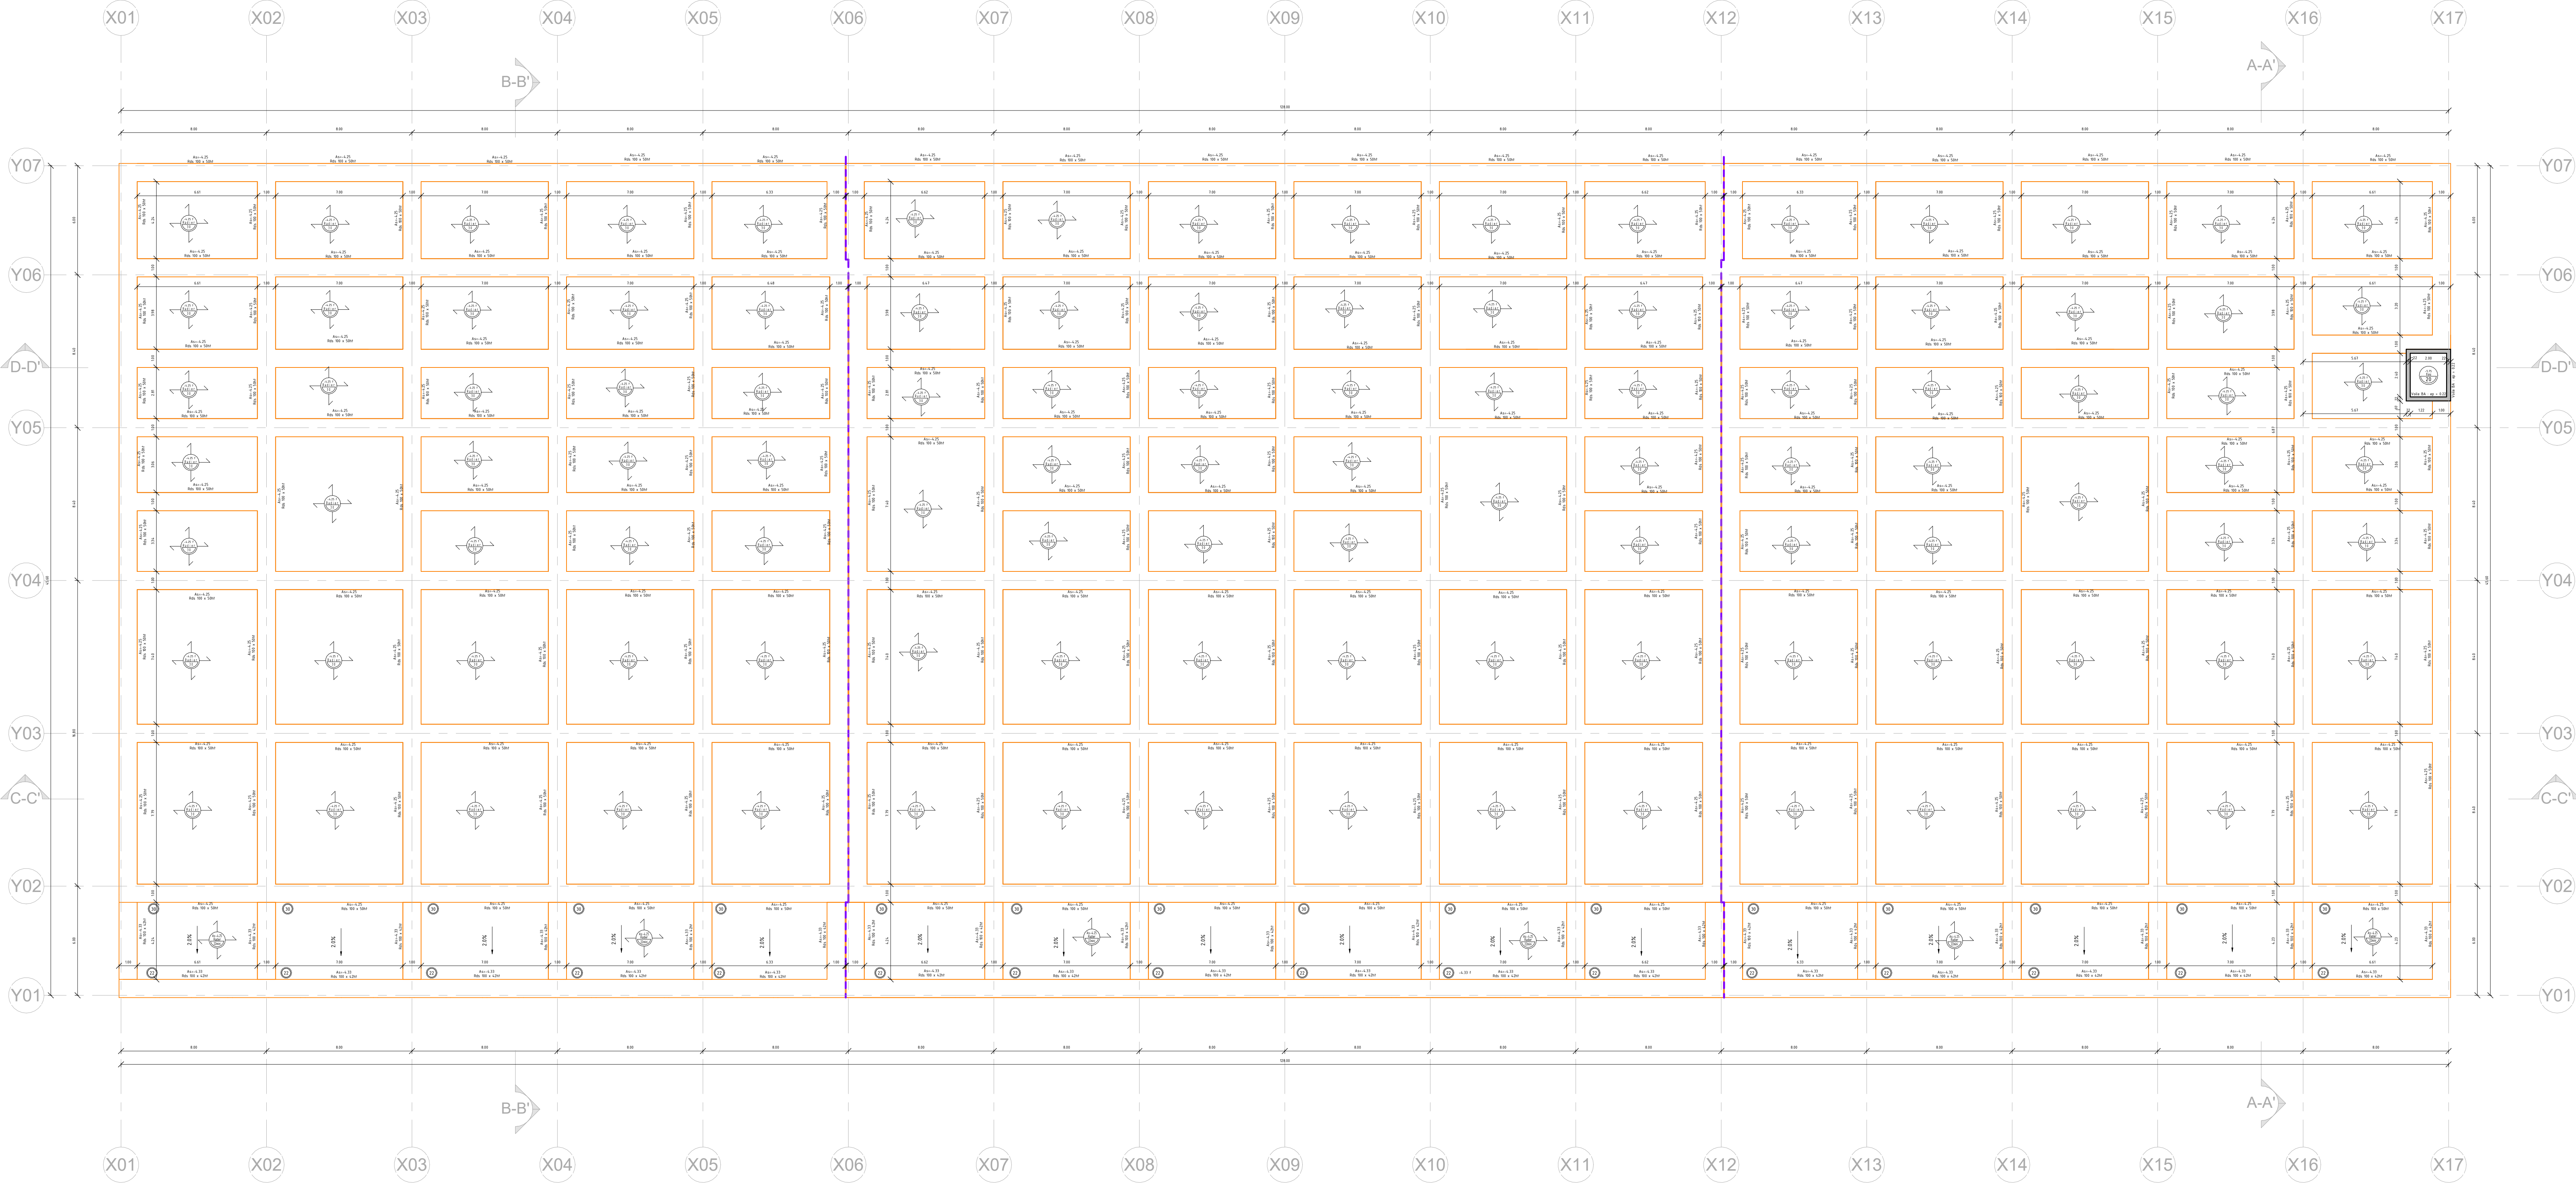


LEGENDE

- Voile en béton armé
- Maçonnerie
- Impact mur voile
- Impact mur maçonnerie
- Acrotère
- Impact Acrotère
- Poteau (Po)
- Impact Poteau
- Joint de dilatation 2cm
- Pu : Poutre
- Raidisseur
- Arase inférieure
- Epaisseur minimale
- Epaisseur de la dalle

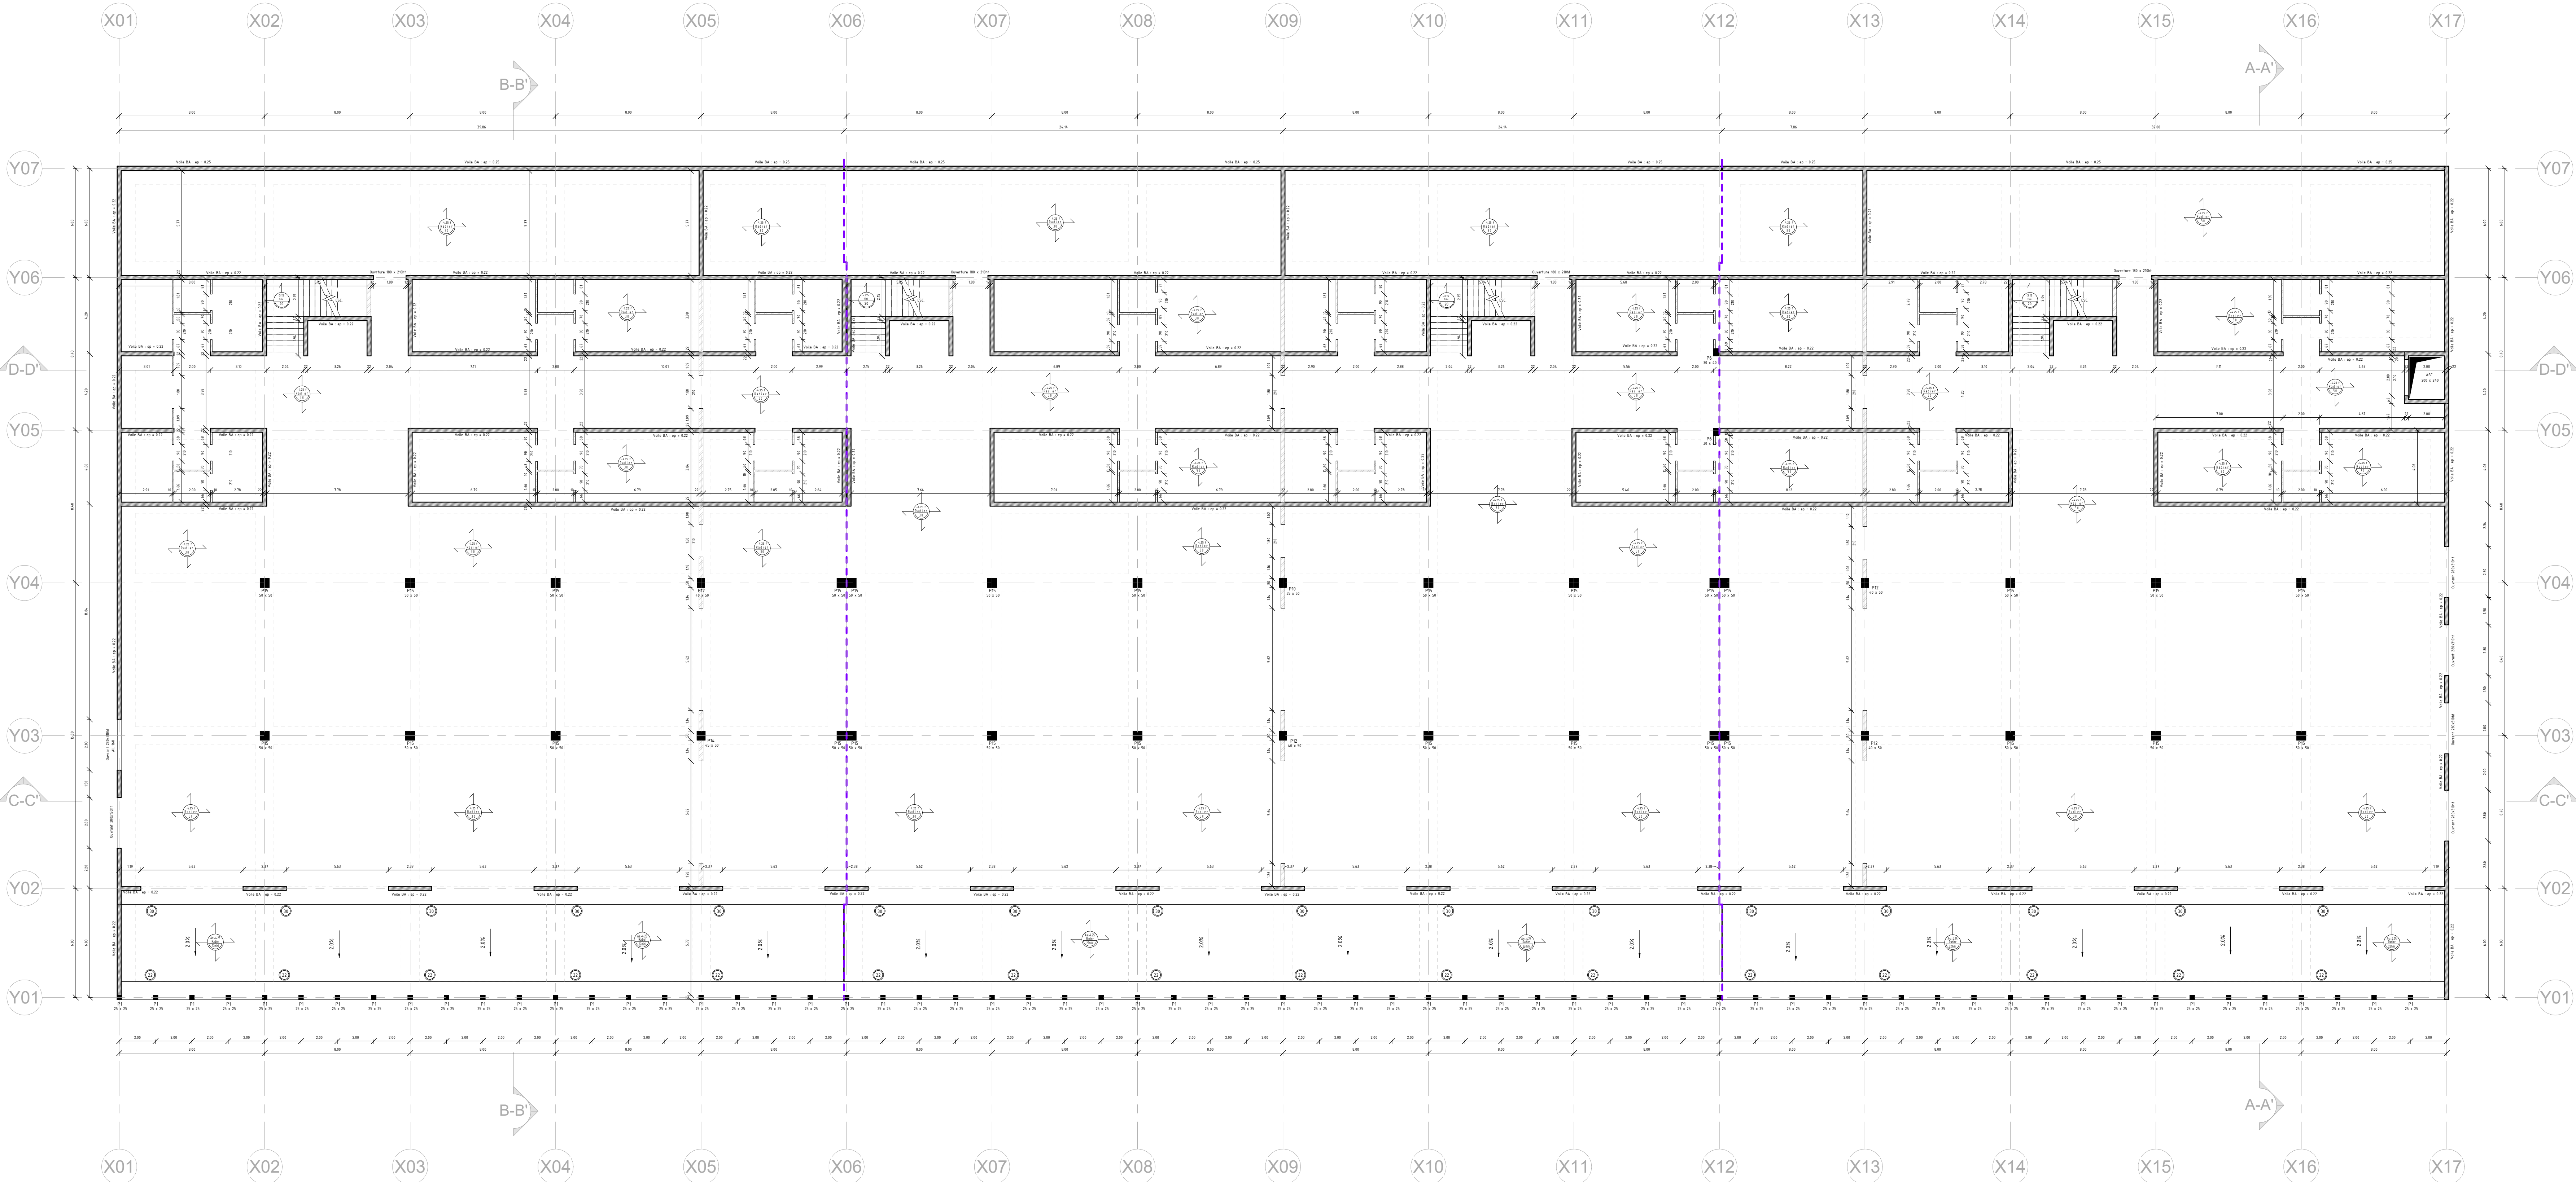


LEGENDE

- Voile en béton armé
- Maçonnerie
- Impact mur voile
- Impact mur maçonnerie
- Acrotère
- Impact Acrotère
- Poteau (Po)
- Impact Poteau
- Joint de dilatation 2cm
- Pu : Poutre
- Raidisseur
- Arase inférieur
- Epaisseur minimale
- 20 Epaisseur de la dalle

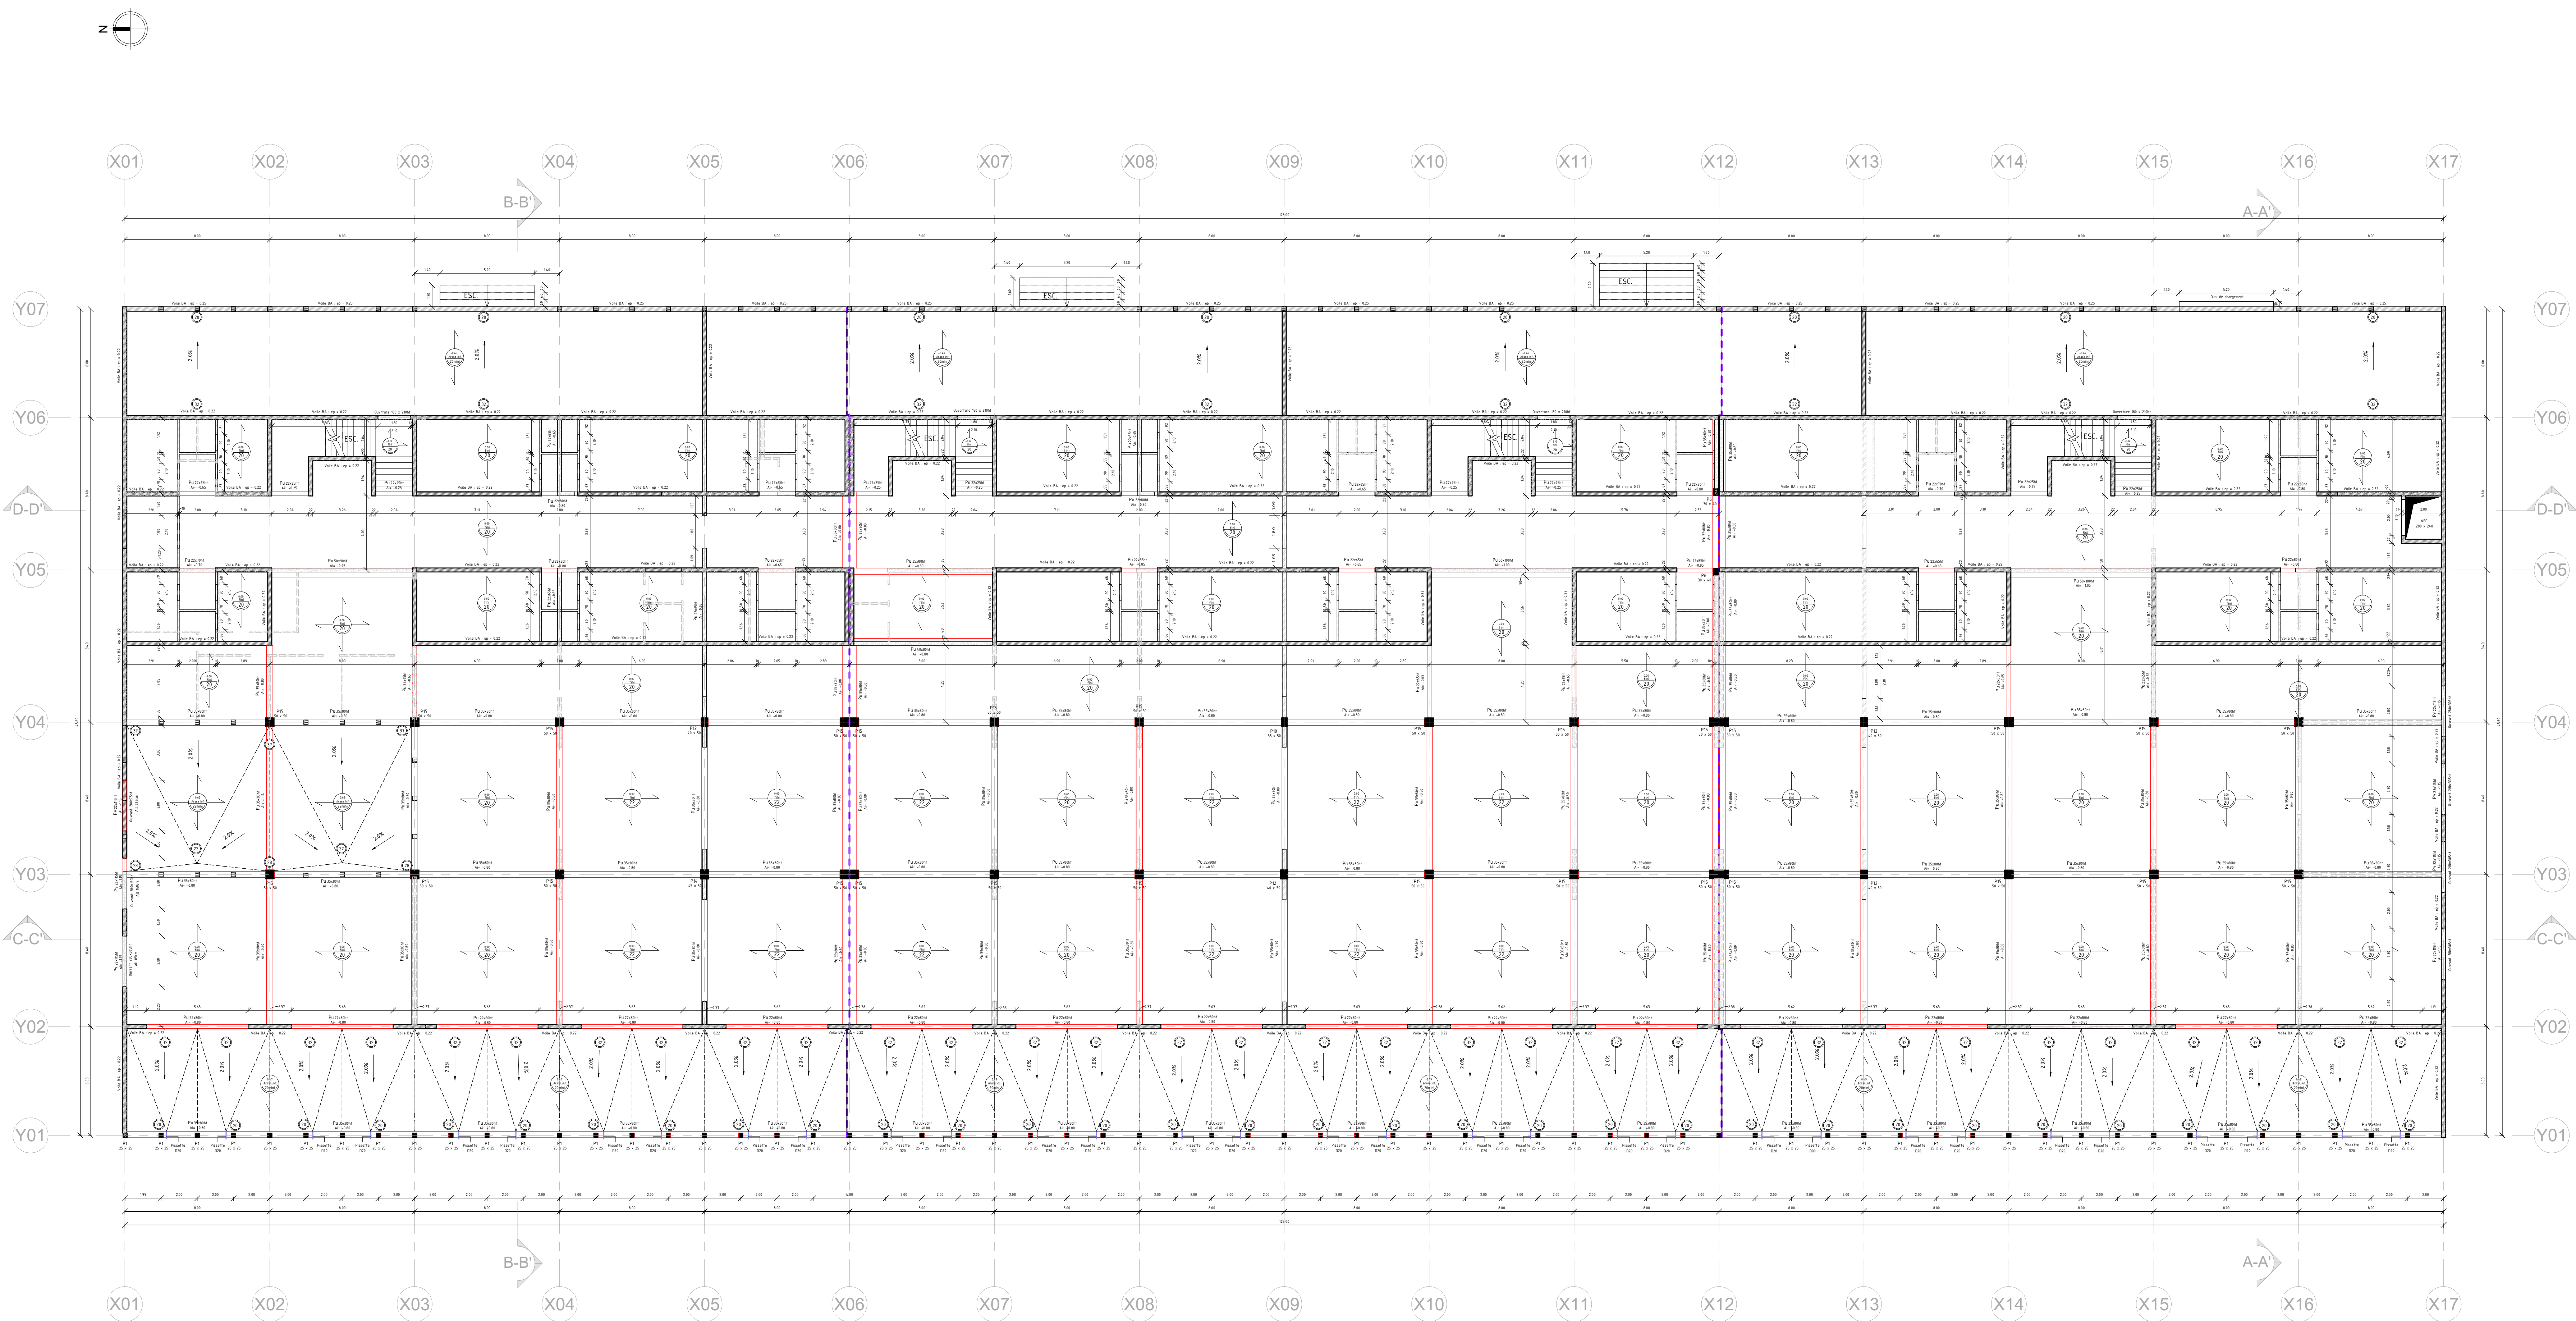

LEGENDE

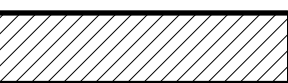

Voile en béton armé



Maçonnerie

Impact mur voile

Impact mur maçonnerie



Acrotère



Impact Acrotère



Poteau (Po)



Impact Poteau

----- Joint de dilatation 2cm



Pu : Poutre



Raidisseur

Arase inférieur



Epaisseur minimale

20 Epaisseur de la dalle





LEGENDE

- Voile en béton armé
- Maçonnerie
- Impact mur voile
- Impact mur maçonnerie
- Acrotère
- Impact Acrotère
- Poteau (Po)
- Impact Poteau
- Joint de dilatation 2cm
- Pu : Poutre
- Raidisseur
- Arase inférieur
- Epaisseur minimale
- Epaisseur de la dalle

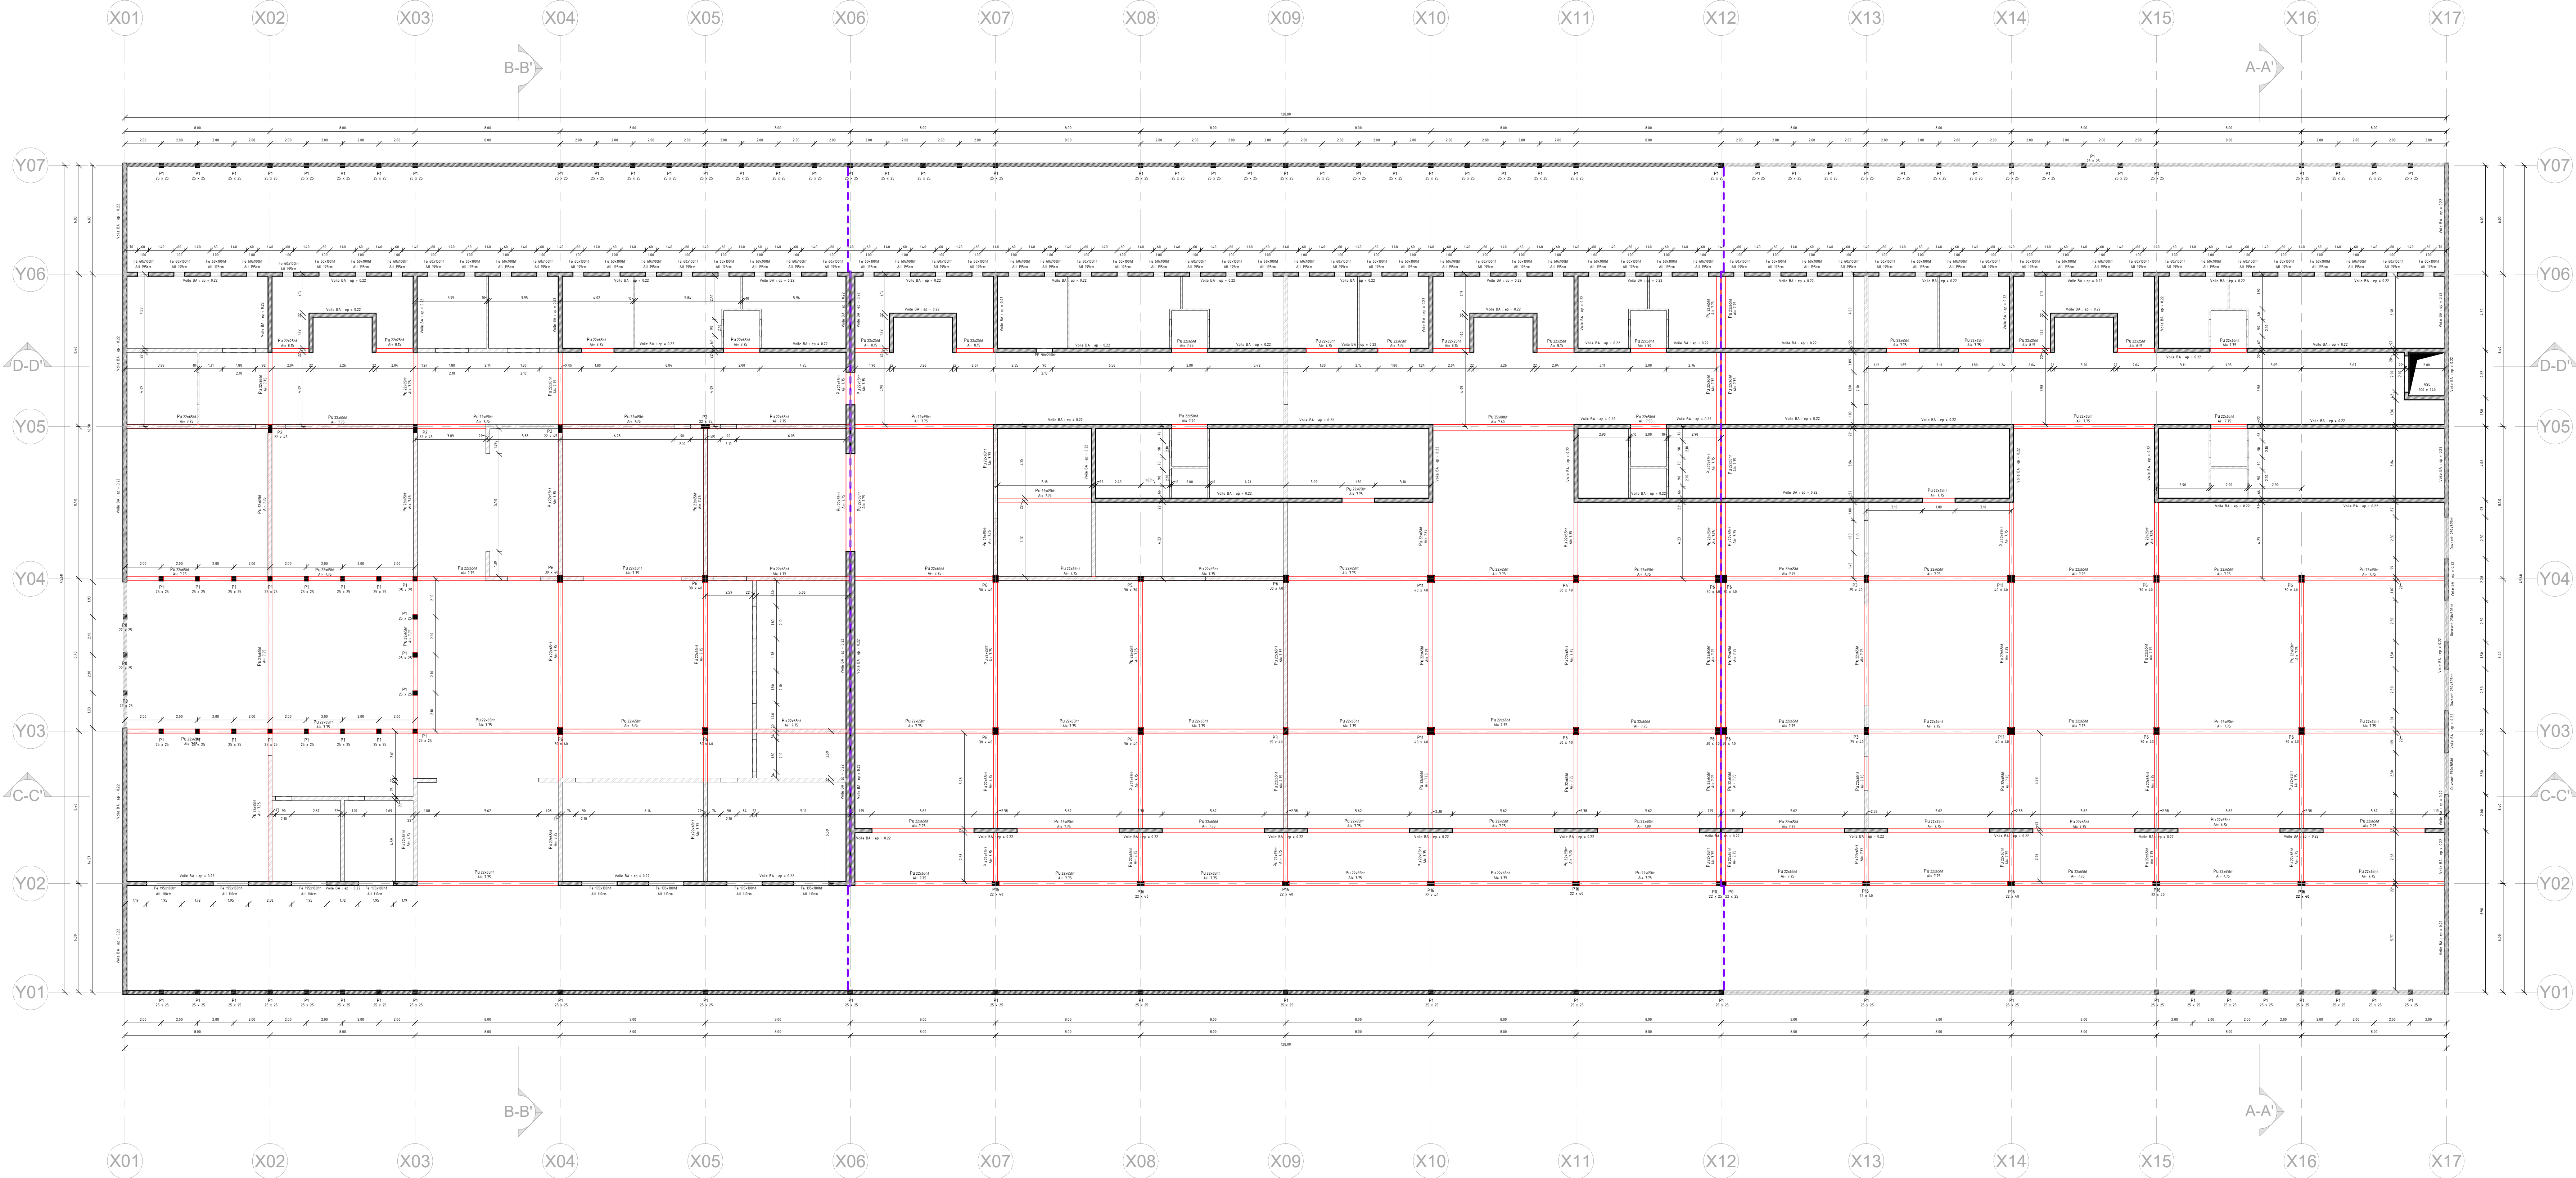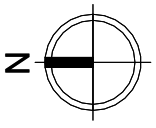

LEGENDE

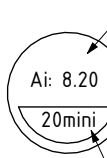
-  Acrotère Ep= 25cm
-  Joint de dilatation 2cm
-  Arase inférieur
-  Epaisseur minimale
-  Epaisseur de la dalle

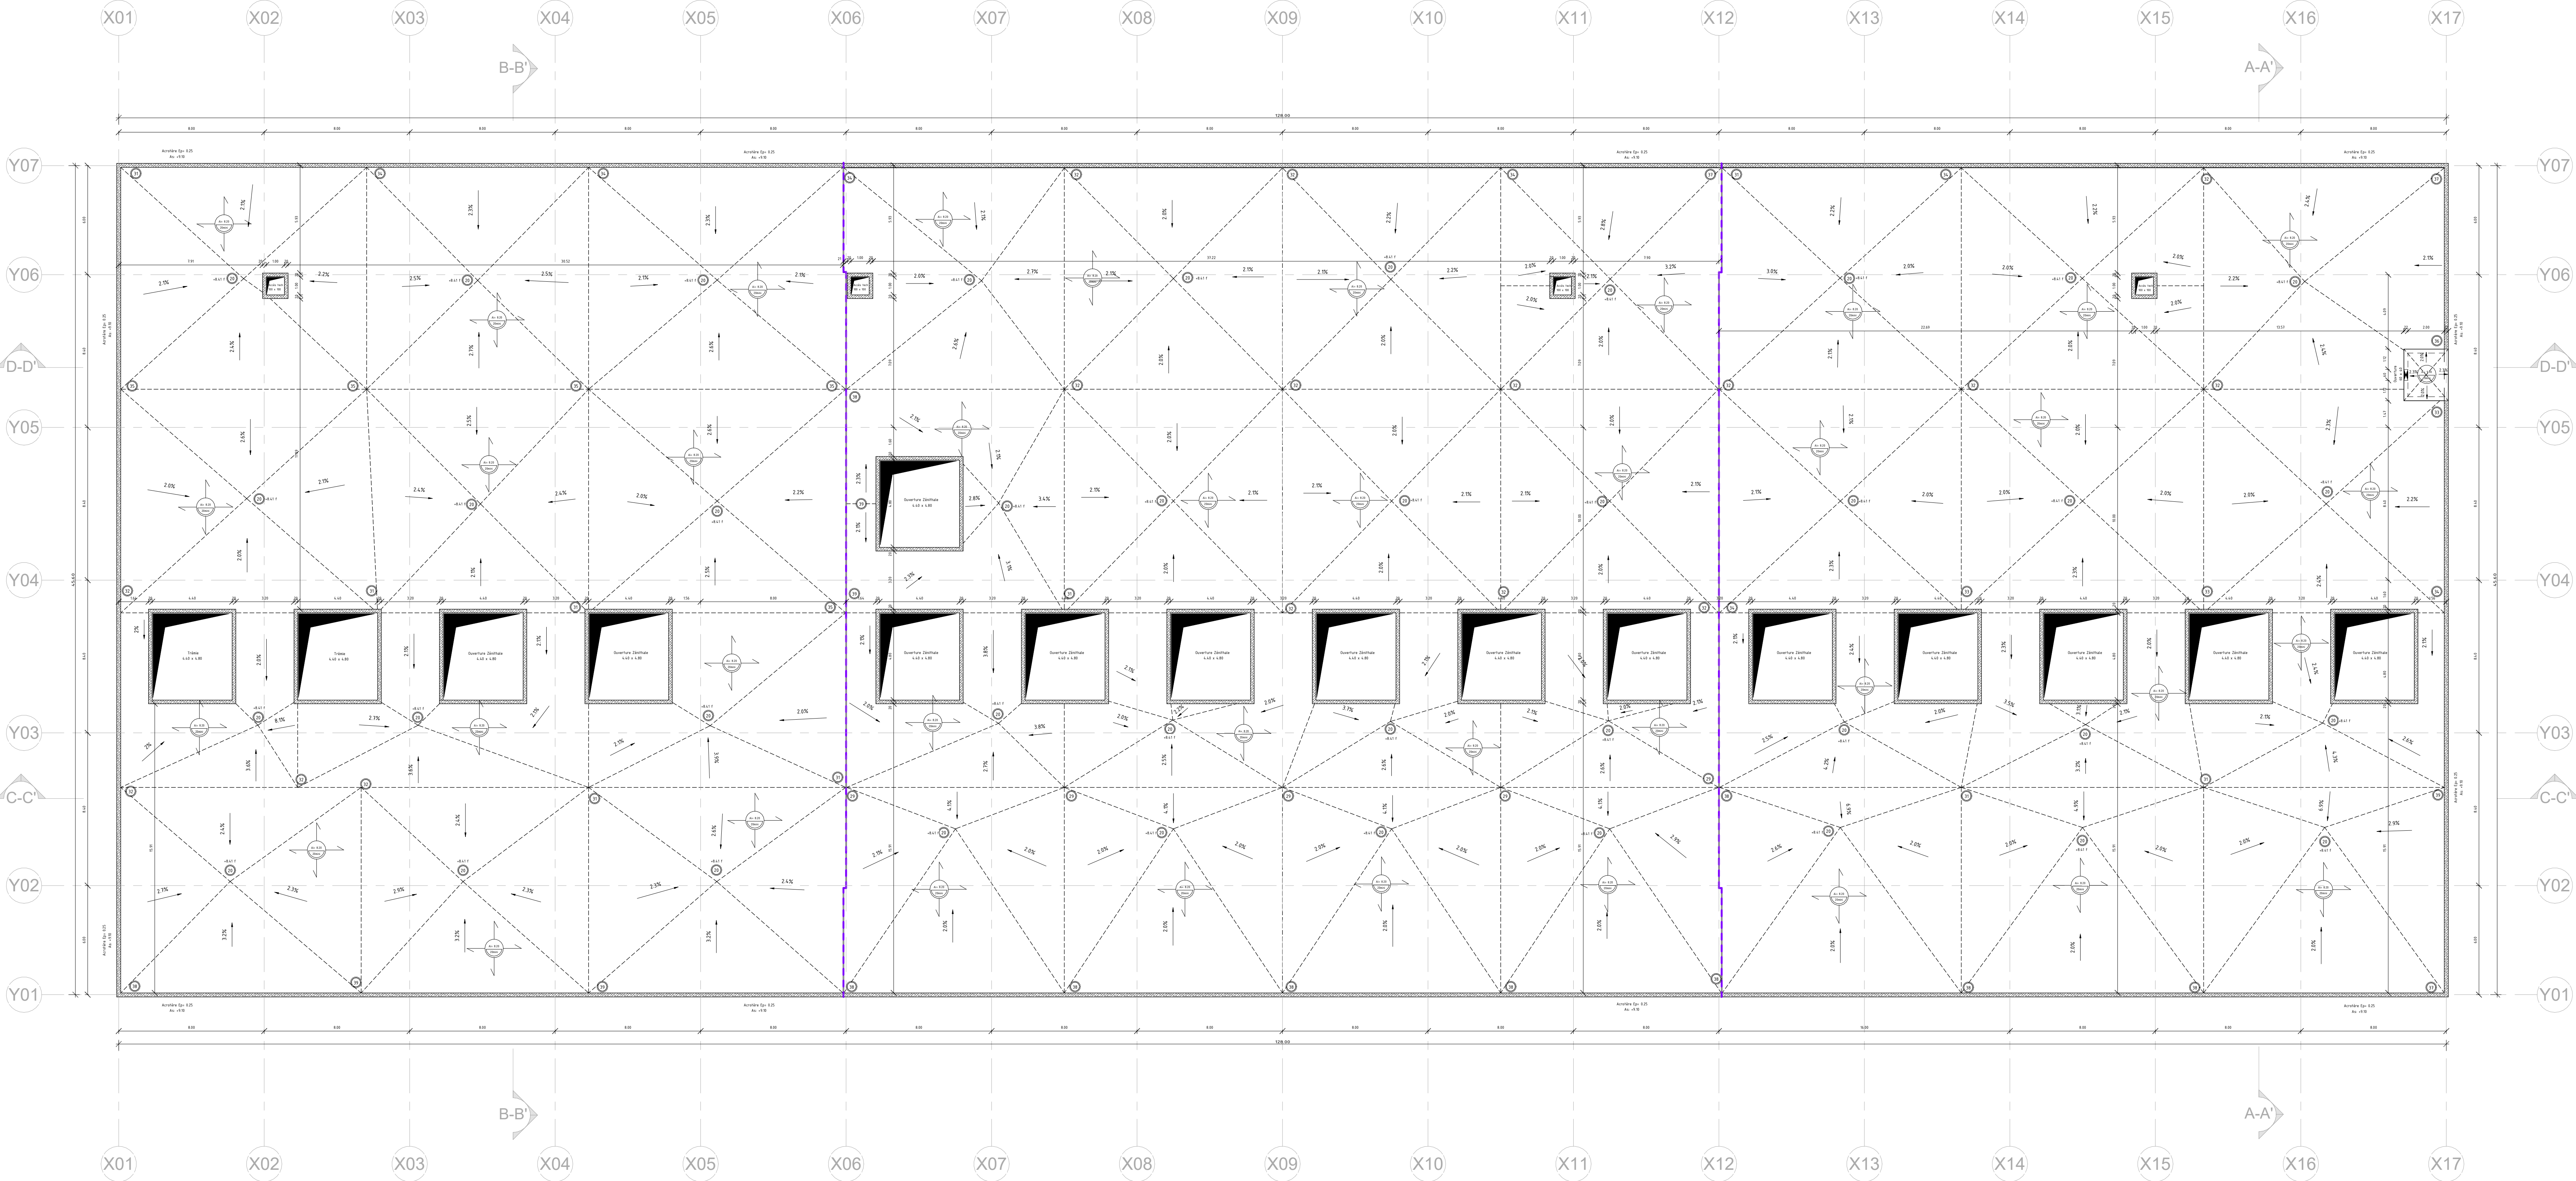


LEGENDE

- Murs
- Dalle
- Joint de dilatation 2cm
- Pu : Poutre
- Rds : Raidisseur

COUPE AA'

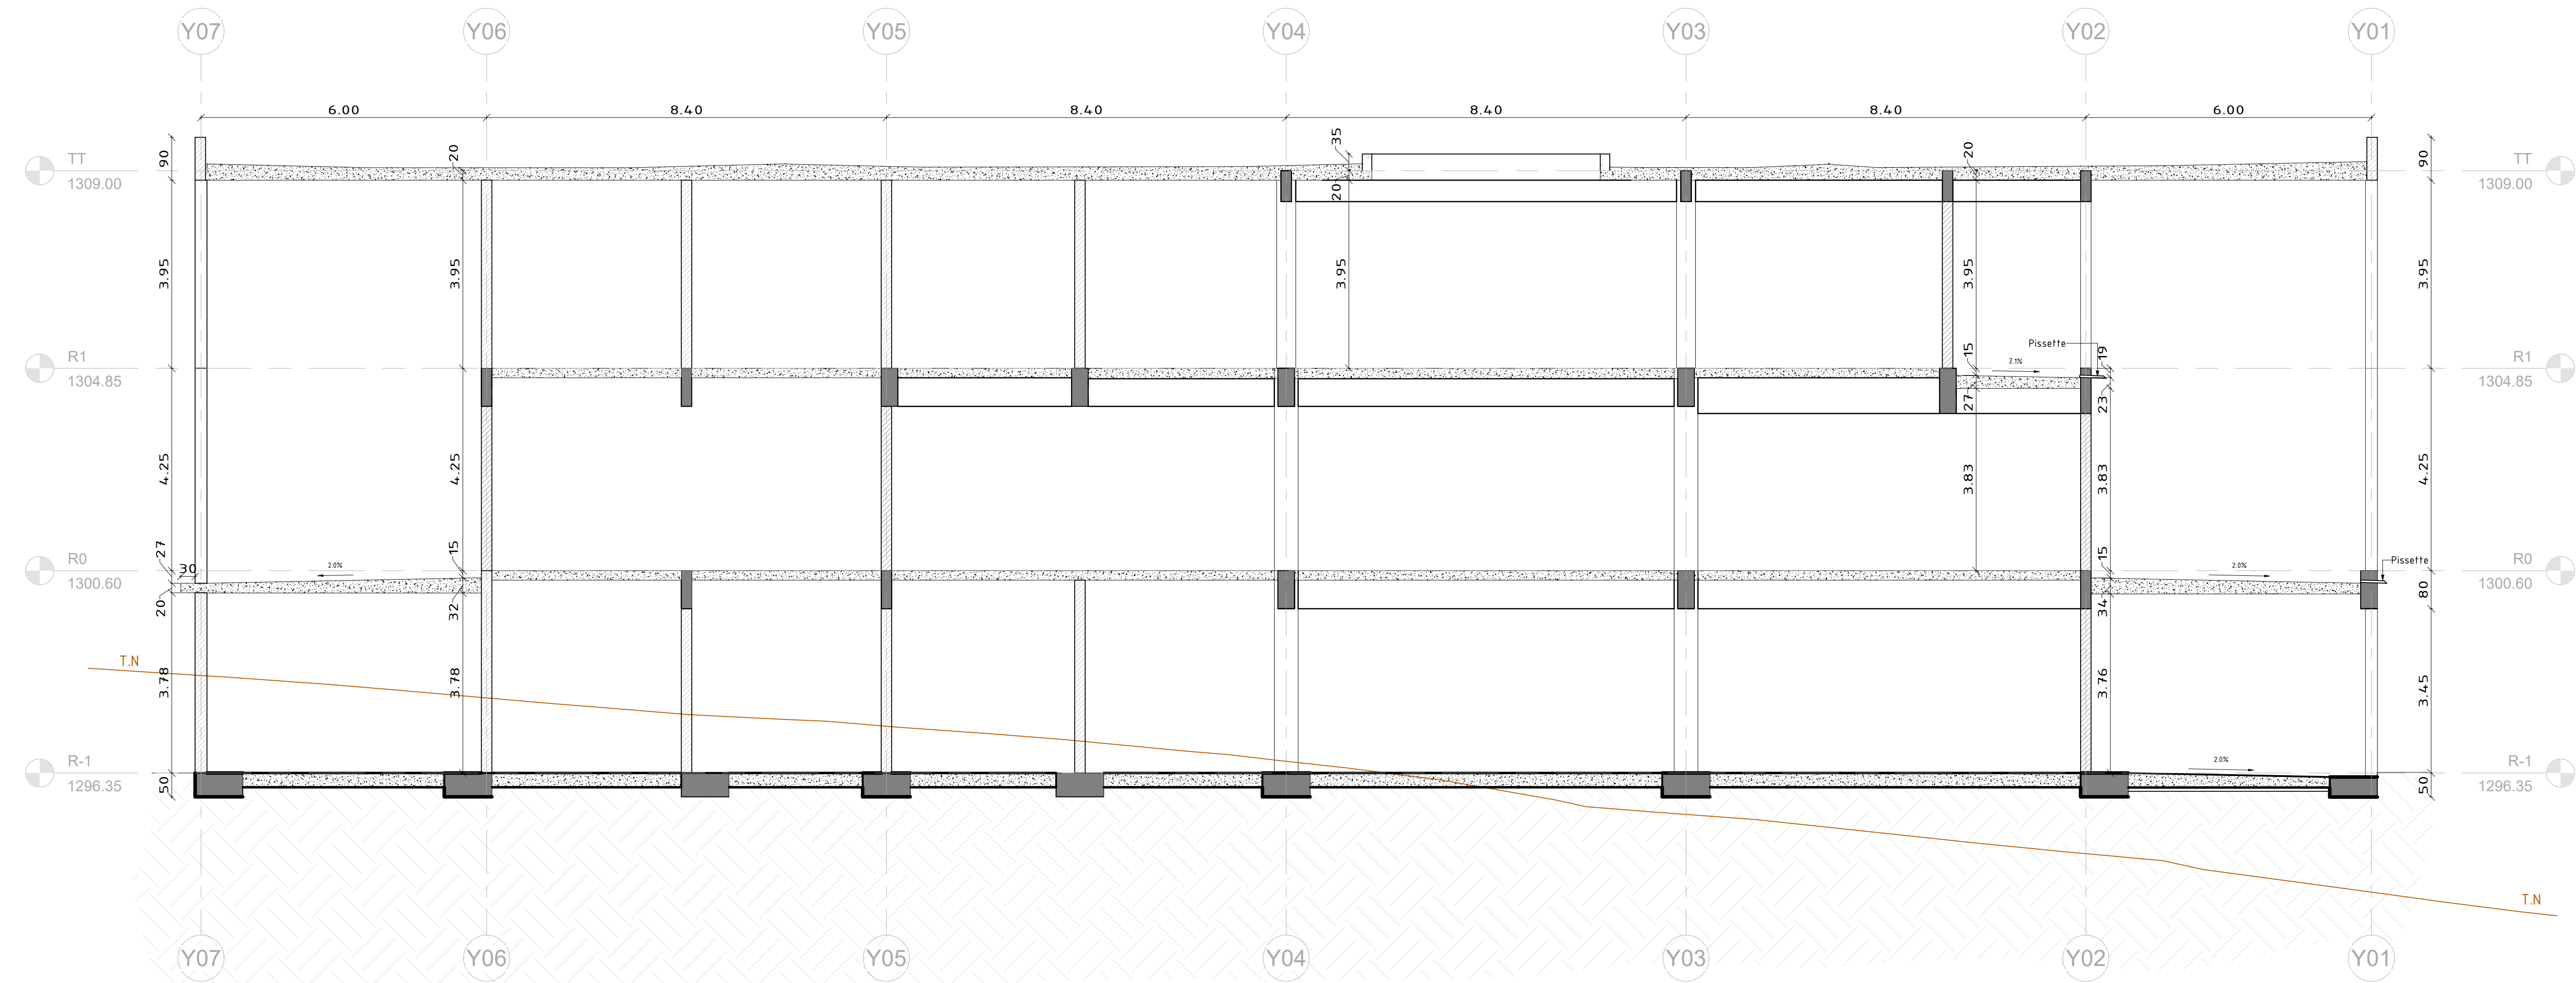


COUPE BB'

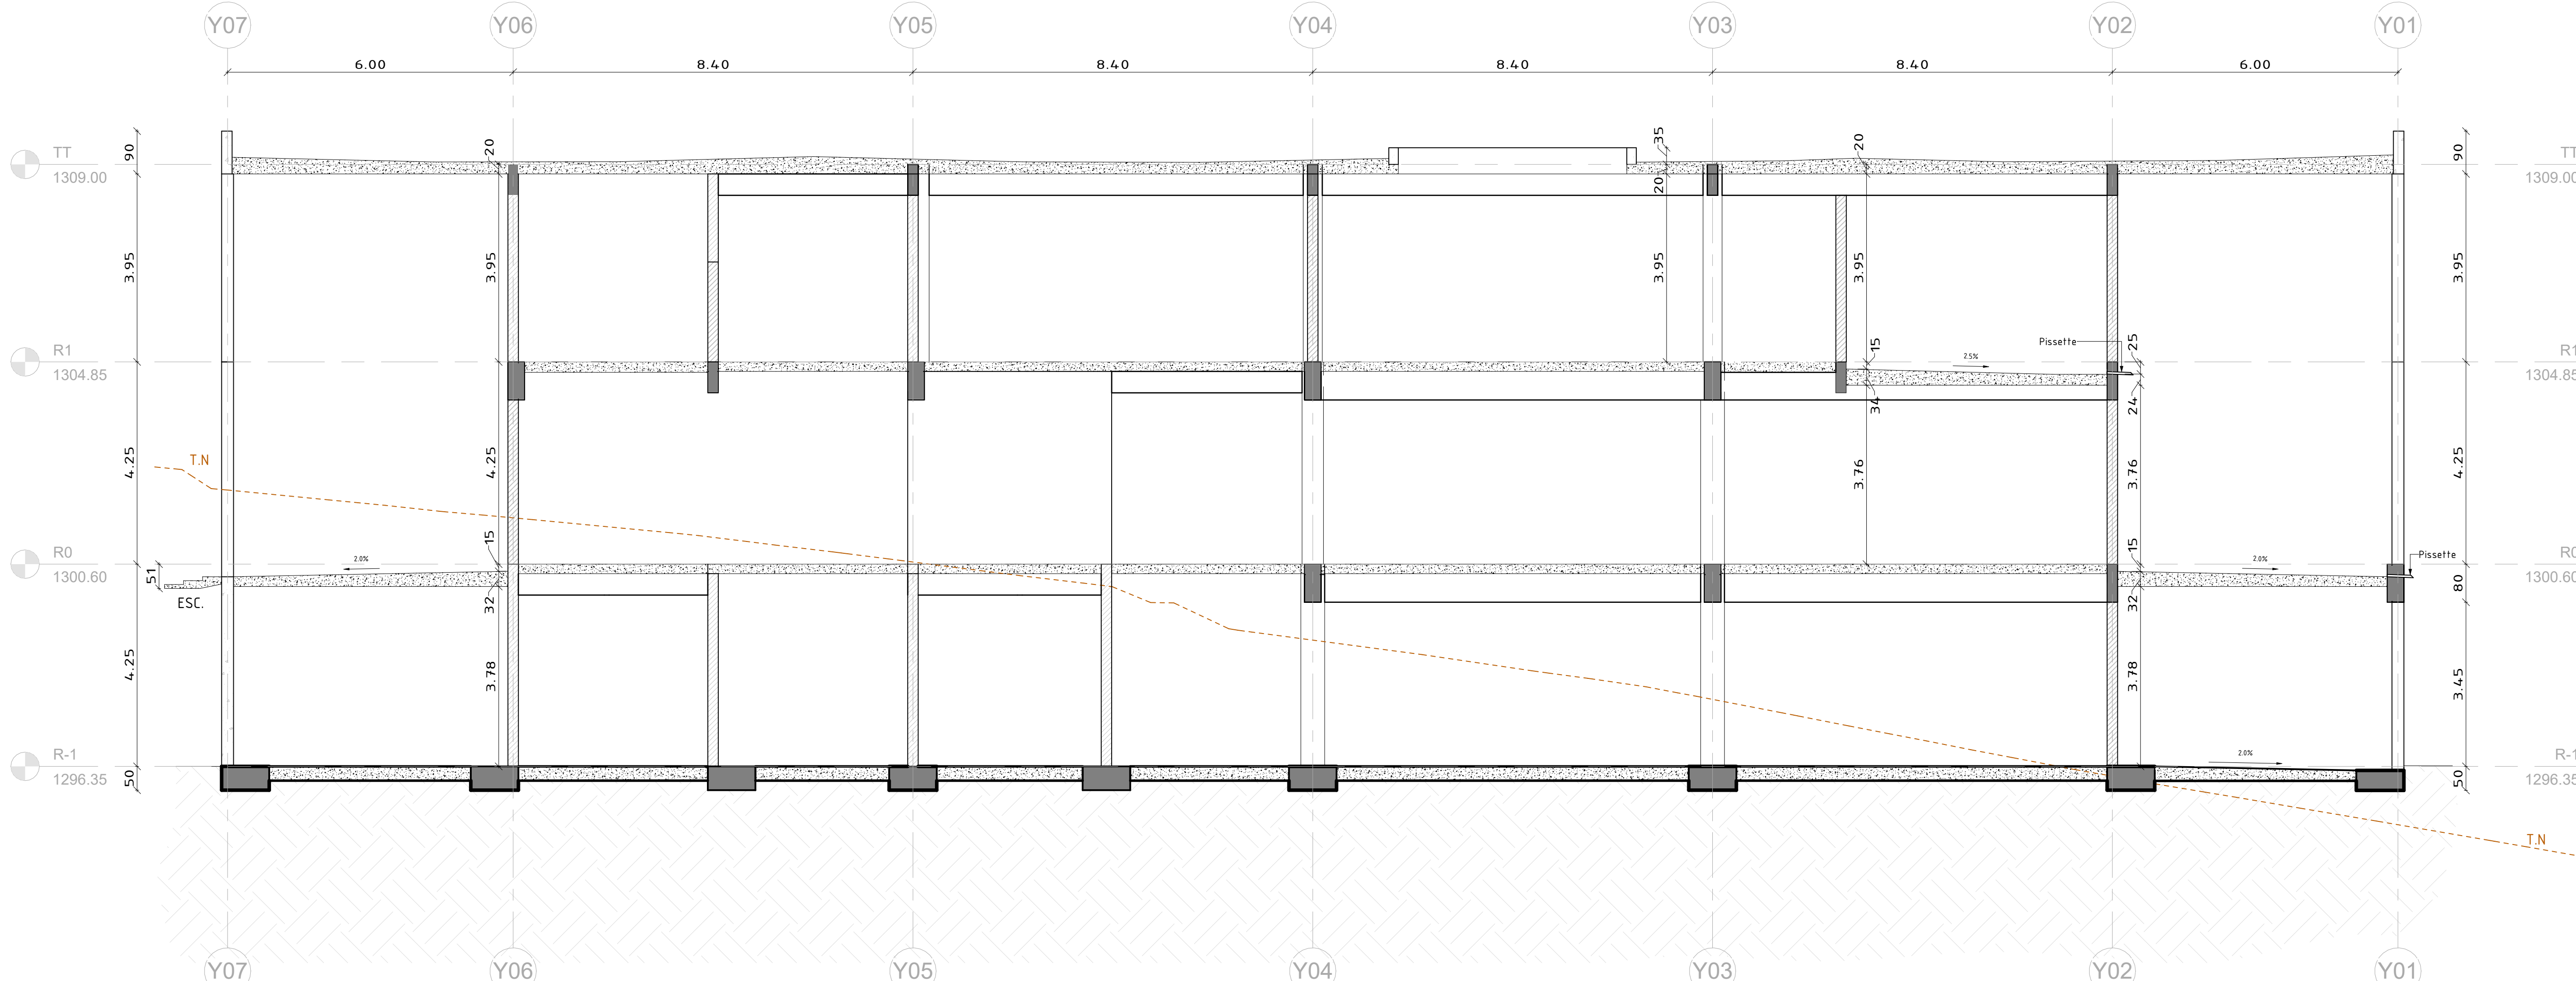

LEGENDE

- Murs
- Dalle
- Joint de dilatation 2cm
- Pu : Poutre
- Rds : Raidisseur

COUPE CC'

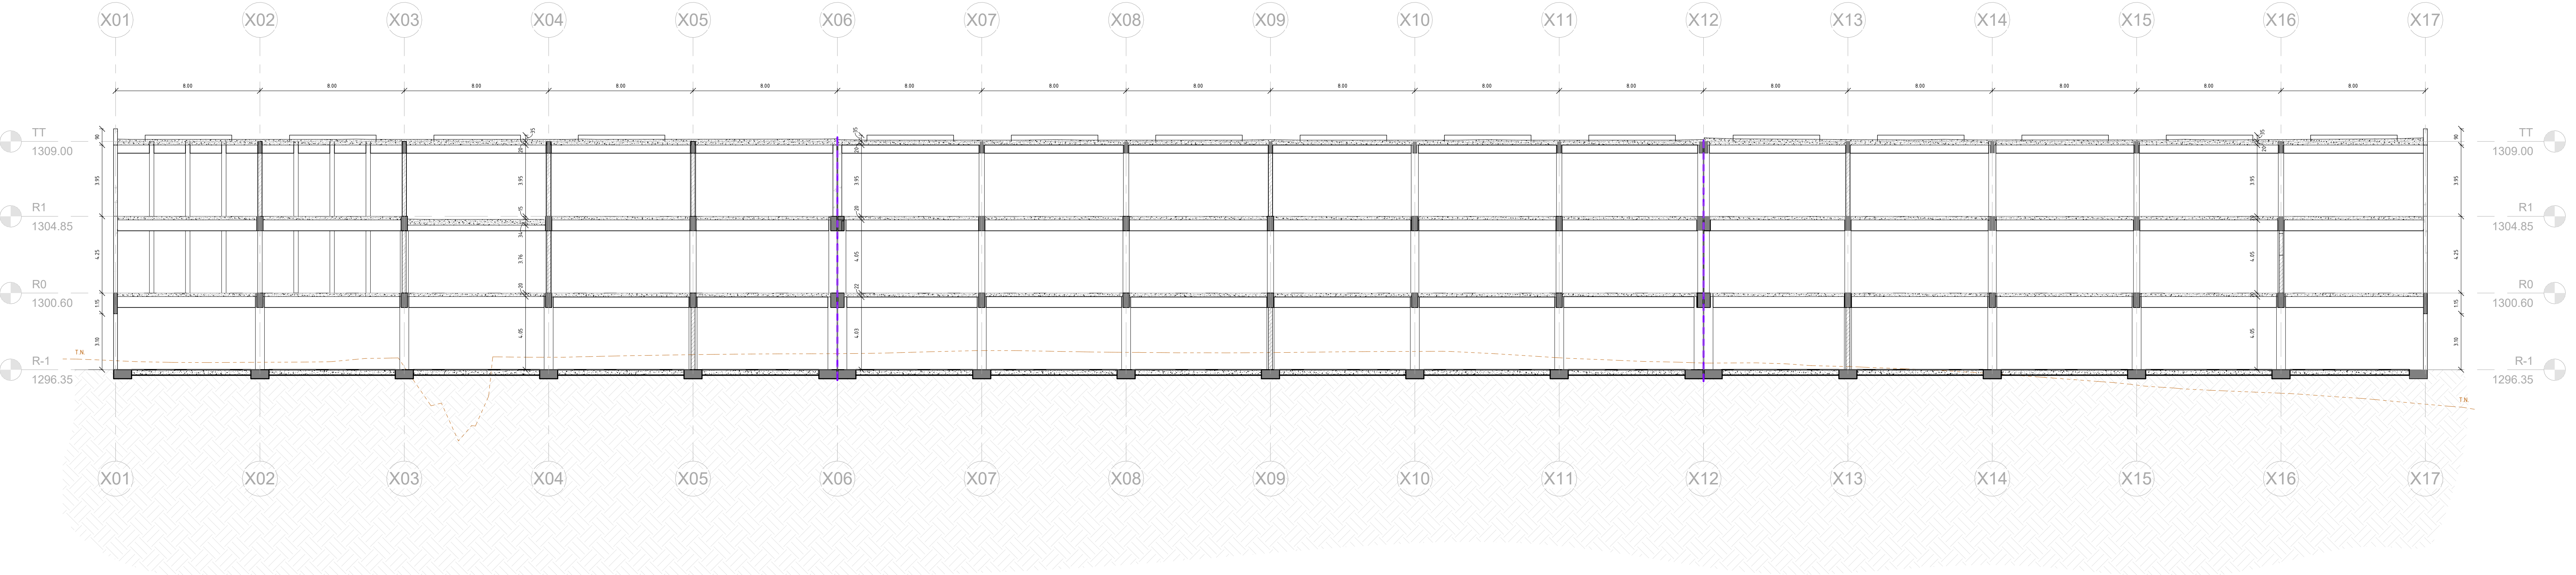

COUPE DD'

